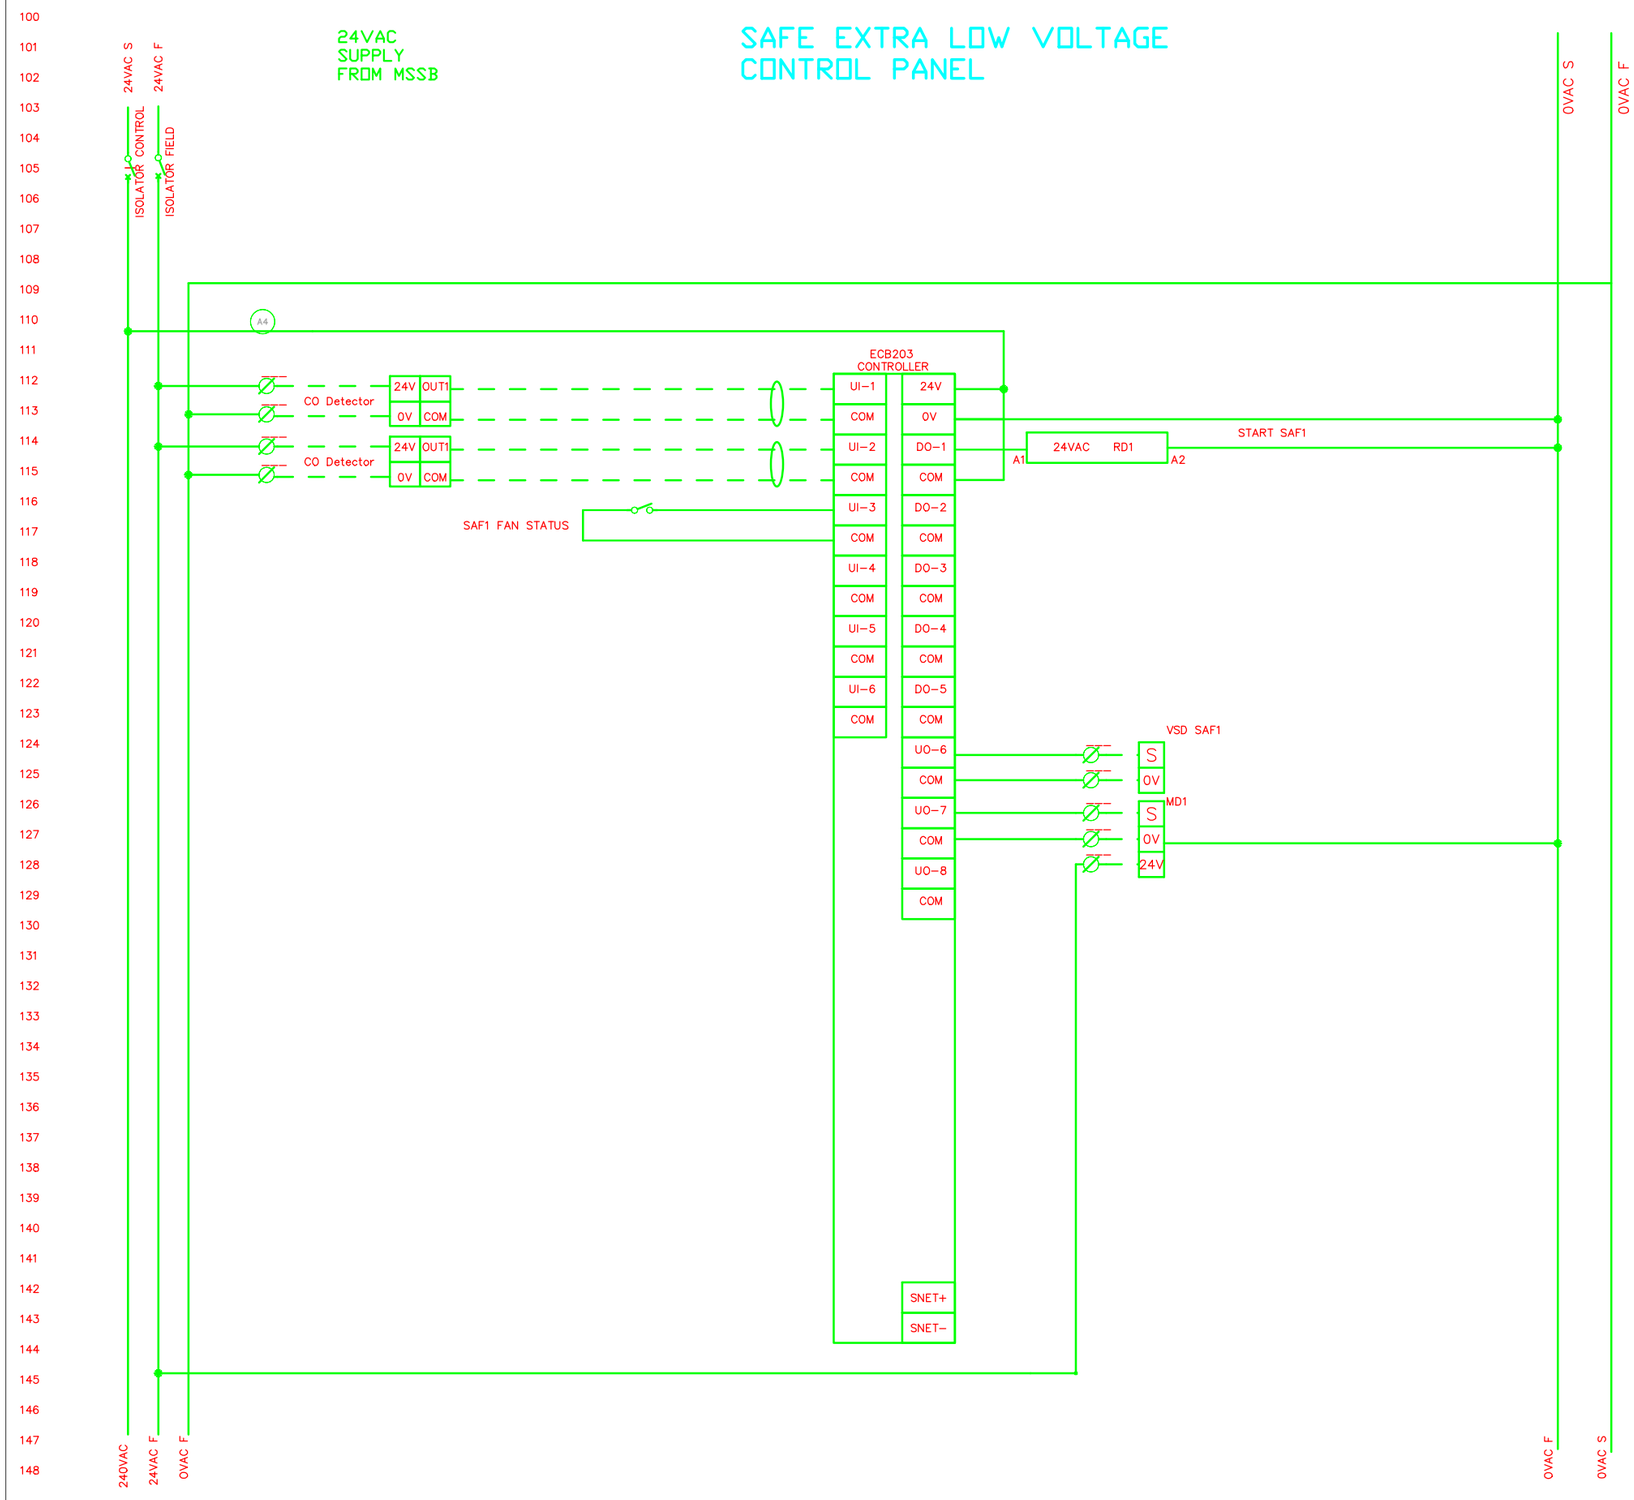

DRAWING TITLE	CONTROL PANEL ELECTRICAL SCHEMATIC - 1.2			
E				DATE 10/11/2016
D				DESIGNED MJS
C				DRAWN MJS
B				SCALE
A	10/11/16	FOR APPROVAL	MJS	SHEET A3
REV	DATE	DESCRIPTION	BY	SHEET No.

PROJECT: AUSTRALIAN FEDERAL POLICE DATA CENTER

CLIENT: BCA CONSULTANTS

CONTACT: controlworks

CONTROLWORKS QLD Pty Ltd
07 3256 8606
SERVICEQLD@CONTROLWORKS.COM.AU
WWW.CONTROLWORKS.COM.AU

DWG No. E02-2